

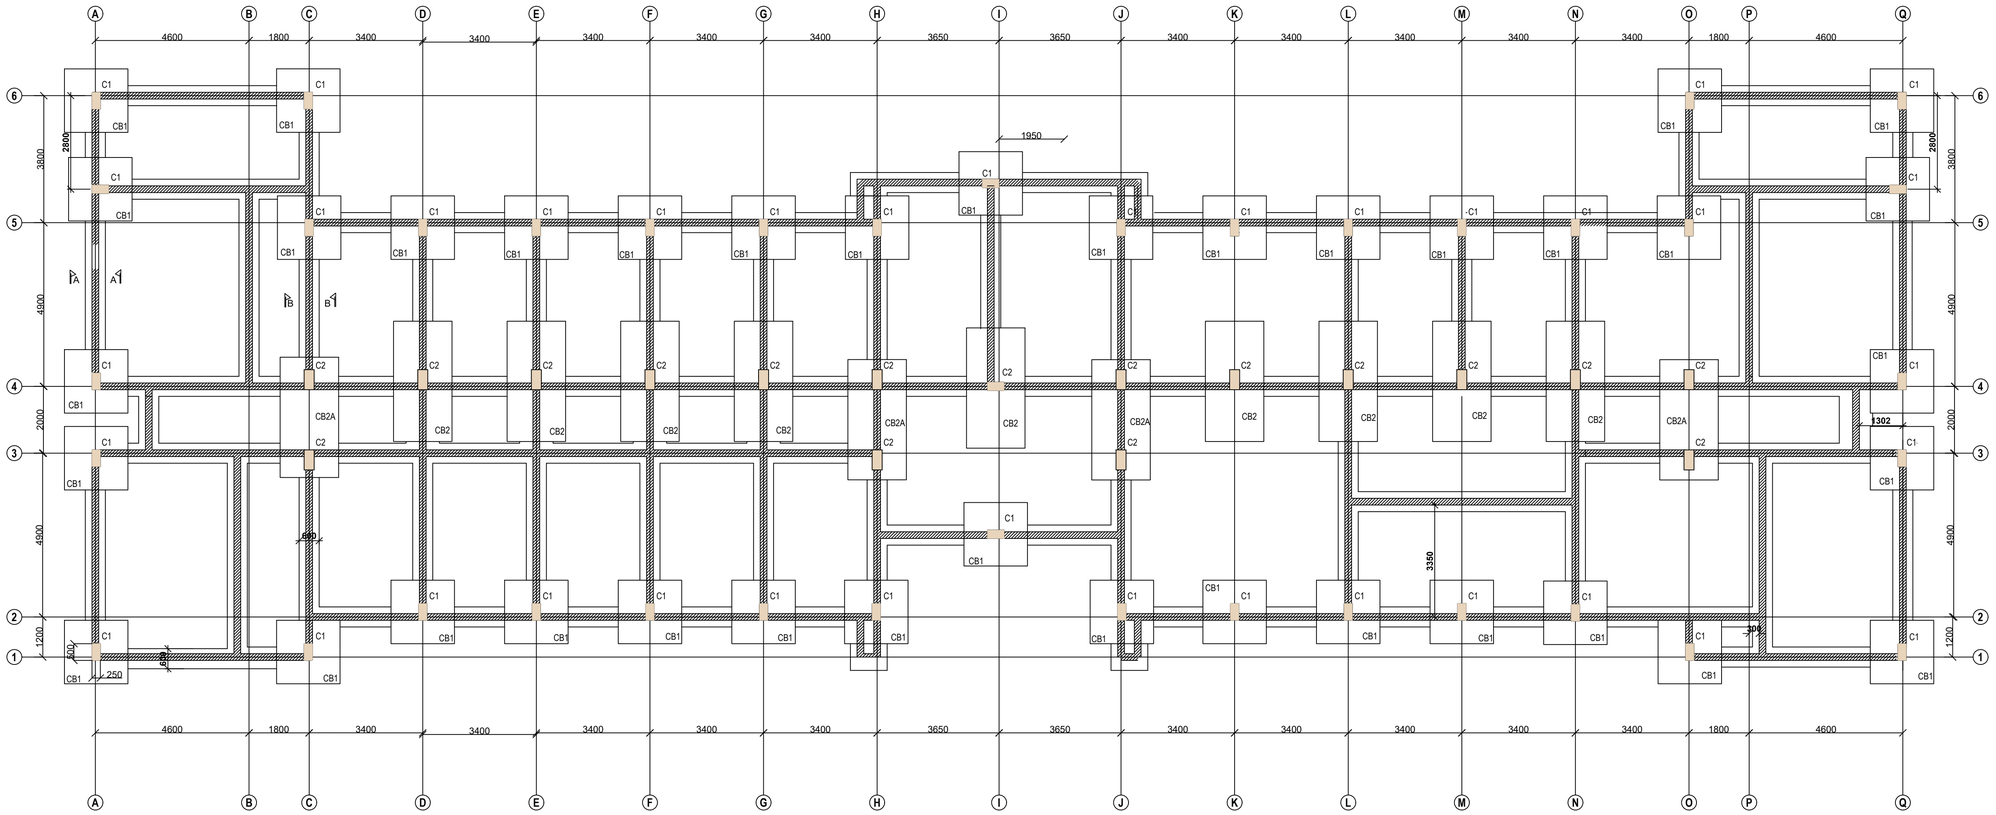



FOUNDATION LAYOUT

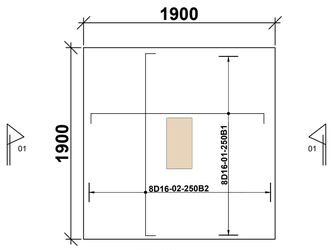


1900X1900X450mm
COLUMN BASE CB1
SCALE 1:25

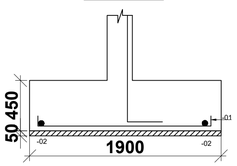


SECTION 01-01
COLUMN BASE CB1
SCALE 1:25

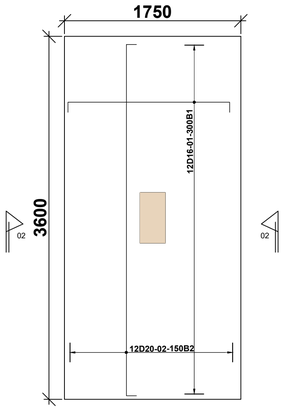


3600X1750X600mm
COLUMN BASE CB2
SCALE 1:25

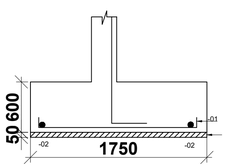


SECTION 02-02
COLUMN BASE CB2
SCALE 1:25

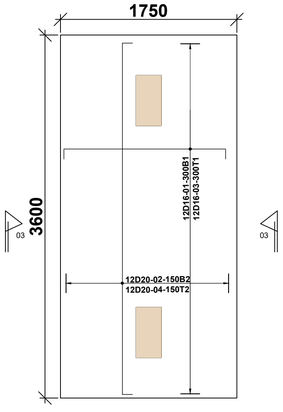


3600X1750X600mm
COLUMN BASE CB2A
SCALE 1:25

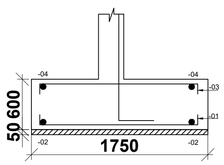


SECTION 03-03
COLUMN BASE CB2A
SCALE 1:25

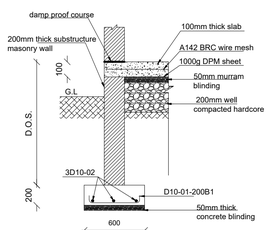



SECTION A-A
EXTERNAL WALL DETAIL
SCALE 1:25

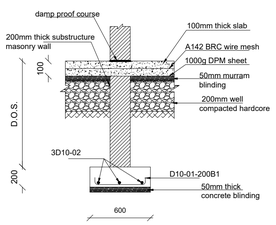

SECTION B-B
INTERNAL WALL DETAIL
SCALE 1:25

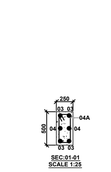

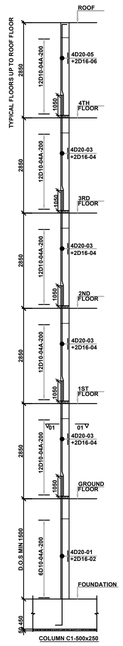

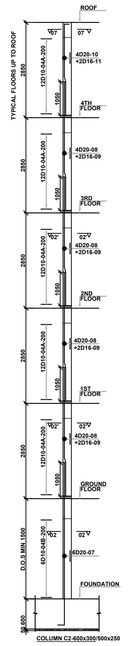

NOTE:

1. Thls design is valid for soils with low bearing capacity (75 - 125 kN/m^2).

NOTES
1. All dimensions are in millimetres unless otherwise stated.
2. All reinforcements must be checked and approved by project structural engineer prior to concreting.
3.All reinforced concrete to be Class 30 mix and blinding concrete to be Class 15 mix.
4. Only figured dimensions to be taken from this drawing.
5. Any descripancy indimensions to be reported to the project consultants i.e architect or engineer.

6. Symbols; T-TMT Rebars to BS 4461: T - Top face B - Bottom face
7. Cover to reinforcement; Slabs - 20mm, Beams - 25mm,Columns - 40mm, Foundations -50mm
8. All structural steel be grade 43A.
9. All welds are 6mm thick.
10. All structural steel to be painted with anti-rust primmer paint.

Client
MINISTRY OF LANDS, PUBLIC WORKS, HOUSING AND URBAN DEVELOPMENT
STATE DEPARTMENT FOR HOUSING AND URBAN DEVELOPMENT

STRUCTURAL ENGINEER:
E.P.L


Designed by: H.I.H | *Checked by: G.N.M*
Approved by: SECRETARY, HOUSING DEPARTMENT
Date: 28TH MARCH 2026 | *Scale: As shown*
Drawing Number: 340 PAX HOSTEL/S01

Project
AFFORDABLE HOUSING G+4_340 PAX HOSTEL STRUCTURAL DRAWINGS (FRAME)

Title FOUNDATION LAYOUT, BASE & RC COLUMN DETAILS

Revisions

No.	Description	Date

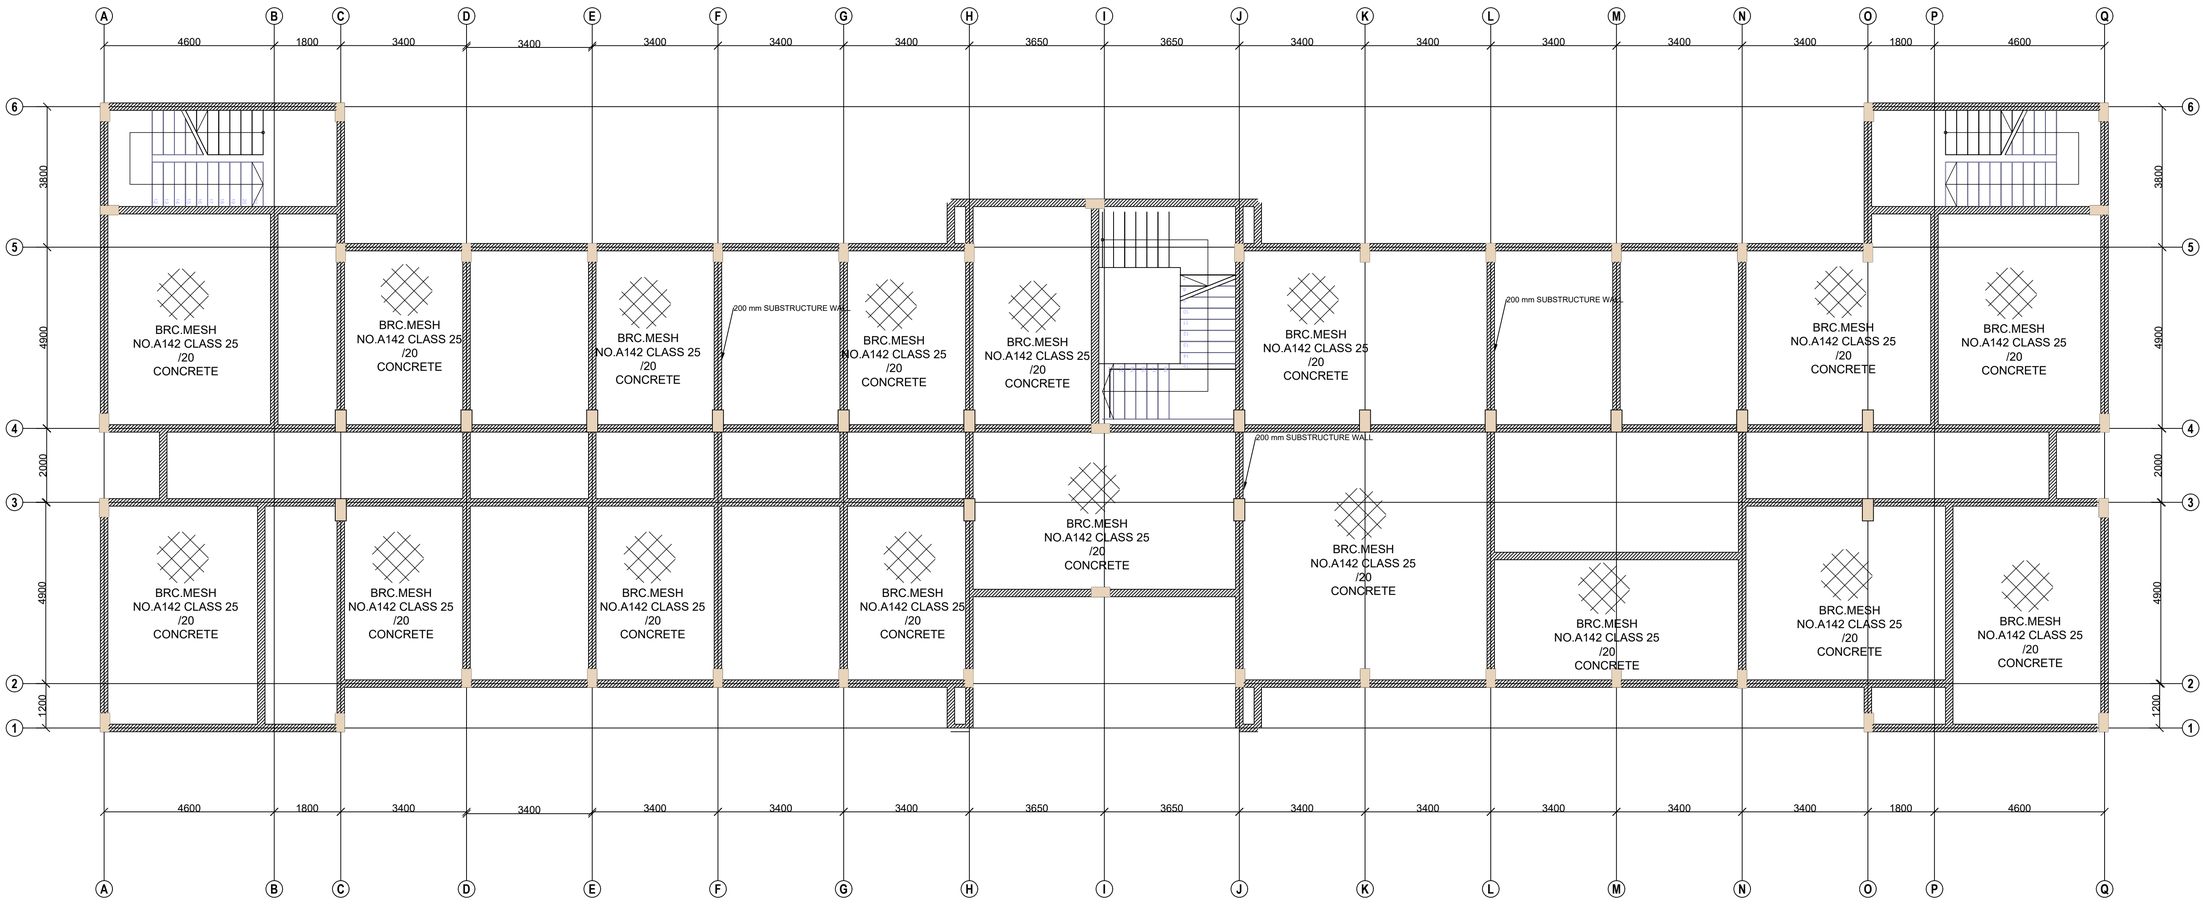

GROUND FLOOR LAYOUT

NOTE:

1. Thls design is valid for soils with low bearing capacity (75 - 125 kN/m^2).

NOTES
1. All dimensions are in millimetres unless otherwise stated.
2. All reinforcements must be checked and approved by project structural engineer prior to concreting.
3.All reinforced concrete to be Class 30 mix and blinding concrete to be Class 15 mix.
4. Only figured dimensions to be taken from this drawing.
5. Any descripancy indimensions to be reported to the project consultants i.e architect or engineer.

6. Symbols; T-TMT Rebars to BS 4461: T - Top face
B - Bottom face
7. Cover to reinforcement; Slabs - 20mm, Beams - 25mm,Columns - 40mm, Foundations -50mm
8. All structural steel be grade 43A.
9. All welds are 6mm thick.
10. All structural steel to be painted with anti-rust primmer paint.

Client
MINISTRY OF LANDS, PUBLIC WORKS, HOUSING AND URBAN DEVELOPMENT
STATE DEPARTMENT FOR HOUSING AND URBAN DEVELOPMENT

STRUCTURAL ENGINEER:
E.P.L


Designed by: H.I.H | *Checked by: G.N.M*
Approved by: SECRETARY, HOUSING DEPARTMENT
Date: 28TH MARCH 2026 | *Scale: As shown*
Drawing Number: 340 PAX HOSTEL/S02

Project
AFFORDABLE HOUSING G+4_340 PAX HOSTEL STRUCTURAL DRAWINGS (FRAME)

Title
GROUND FLOOR LAYOUT

Revisions

No.	Description	Date

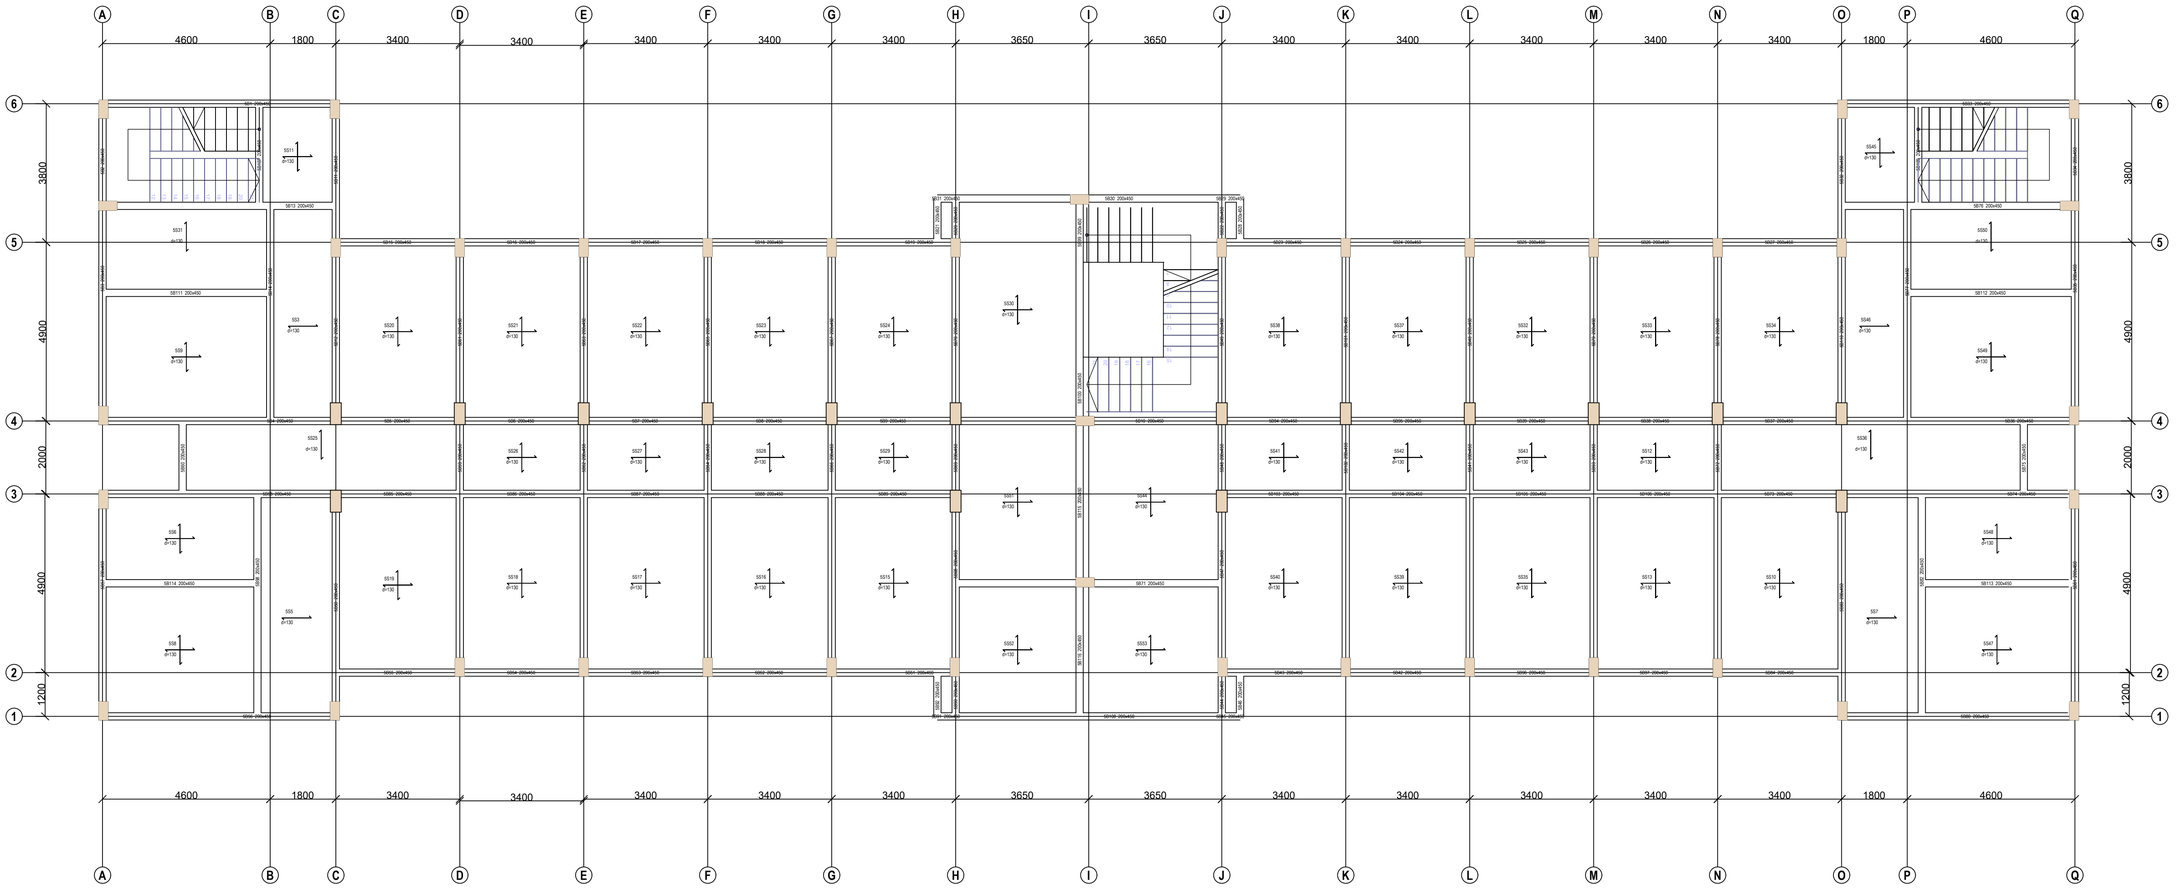

TYPICAL FLOOR LAYOUT

NOTE:

1. THIs design is valid for soils with low bearing capacity (75 - 125 kN/m^2).

NOTES
1. All dimensions are in millimetres unless otherwise stated.
2. All reinforcements must be checked and approved by project structural engineer prior to concreting.
3.All reinforced concrete to be Class 30 mix and blinding concrete to be Class 15 mix.
4. Only figured dimensions to be taken from this drawing.
5. Any descripancy indimensions to be reported to the project consultants i.e architect or engineer.

6. Symbols; T-TMT Rebars to BS 4461: T - Top face
B - Bottom face
7. Cover to reinforcement; Slabs - 20mm,
Beams - 25mm,Columns - 40mm, Foundations -50mm
8. All structural steel be grade 43A.
9. All welds are 6mm thick.
10. All structural steel to be painted with anti-rust primmer paint.

Client
MINISTRY OF LANDS, PUBLIC WORKS, HOUSING AND URBAN DEVELOPMENT

STATE DEPARTMENT FOR HOUSING AND URBAN DEVELOPMENT

STRUCTURAL ENGINEER:

E.P.L

Designed by: H.I.H | *Checked by: G.N.M*

Approved by: SECRETARY, HOUSING DEPARTMENT

Date: 28TH MARCH 2026 | *Scale: As shown*


Drawing Number: 340 PAX HOSTEL/S03

Project
AFFORDABLE HOUSING G+4_340 PAX HOSTEL STRUCTURAL DRAWINGS (FRAME)

Title
TYPICAL FLOOR & BEAM LAYOUT

Revisions

No.	Description	Date

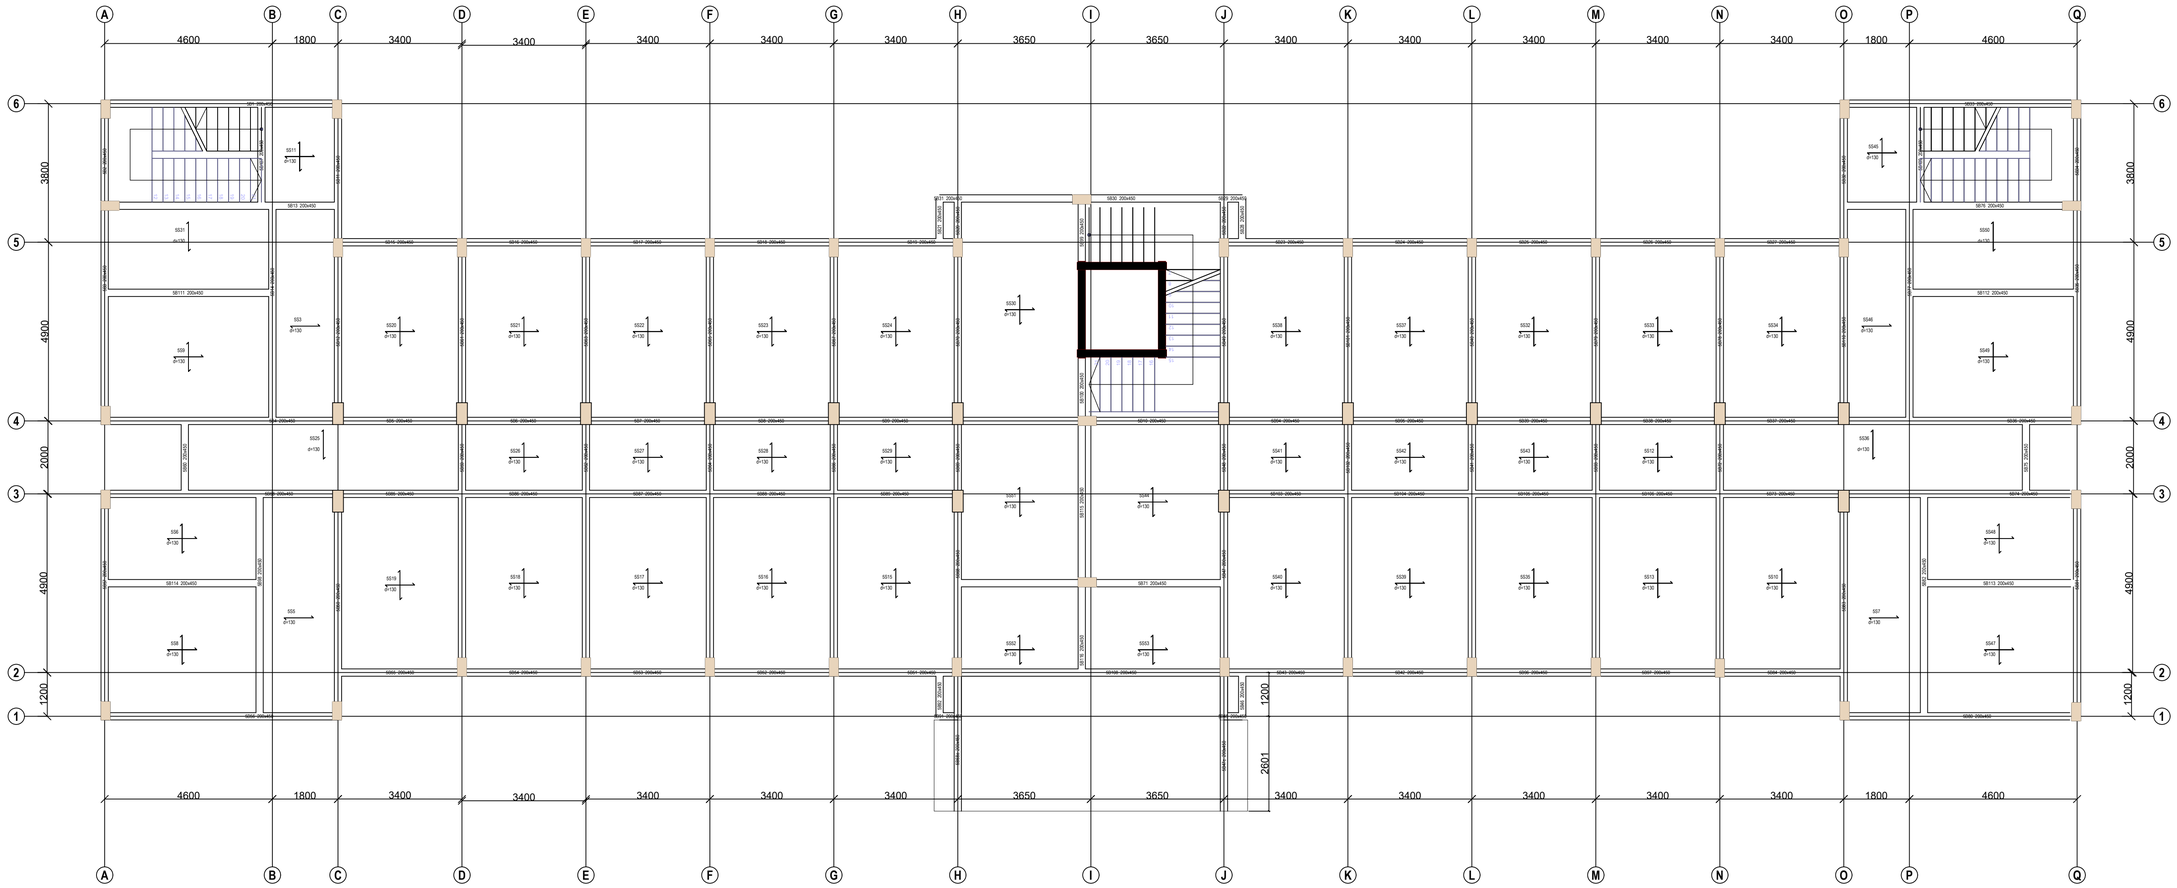

TYPICAL 1st FLOOR LAYOUT

NOTE:

1. Thls design is valid for soils with low bearing capacity (75 - 125 kN/m^2).

NOTES
1. All dimensions are in millimetres unless otherwise stated.
2. All reinforcements must be checked and approved by project structural engineer prior to concreting.
3.All reinforced concrete to be Class 30 mix and blinding concrete to be Class 15 mix.
4. Only figured dimensions to be taken from this drawing.
5. Any descripancy indimensions to be reported to the project consultants i.e architect or engineer.

6. Symbols; T-TMT Rebars to BS 4461: T - Top face B - Bottom face
7. Cover to reinforcement; Slabs - 20mm, Beams - 25mm,Columns - 40mm, Foundations -50mm
8. All structural steel be grade 43A.
9. All welds are 6mm thick.
10. All structural steel to be painted with anti-rust primmer paint.

Client
MINISTRY OF LANDS, PUBLIC WORKS, HOUSING AND URBAN DEVELOPMENT
STATE DEPARTMENT FOR HOUSING AND URBAN DEVELOPMENT

STRUCTURAL ENGINEER:
E.P.L


Designed by: H.I.H | *Checked by: G.N.M*
Approved by: SECRETARY, HOUSING DEPARTMENT
Date: 28TH MARCH 2026 | *Scale: As shown*
Drawing Number: 580 PAX HOSTEL/S03

Project
AFFORDABLE HOUSING G+4_340 PAX HOSTEL STRUCTURAL DRAWINGS (FRAME)

Title
TYPICAL 1st FLOOR & BEAM LAYOUT

Revisions

No.	Description	Date

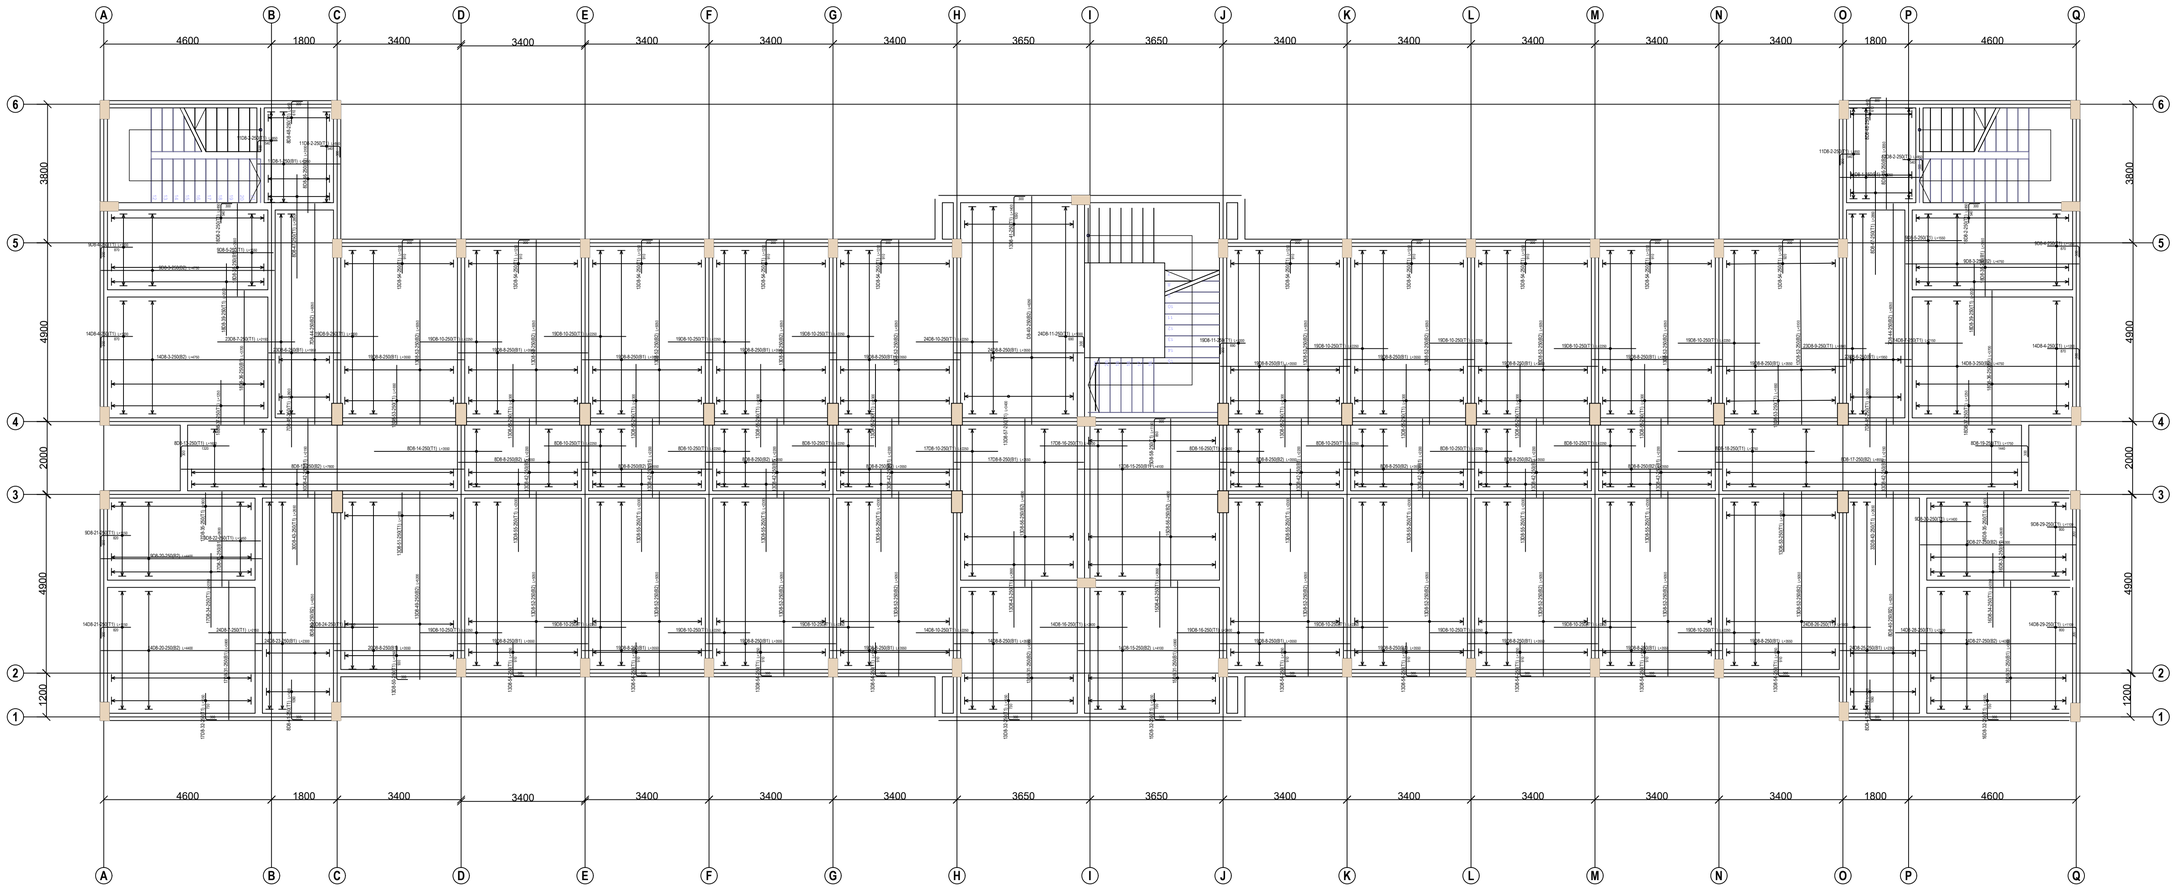

TYPICAL RC SLAB DETAILS

NOTE:

1. THIs design is valid for soils with low bearing capacity (75 - 125 kN/m^2).

NOTES
1. All dimensions are in millimetres unless otherwise stated.
2. All reinforcements must be checked and approved by project structural engineer prior to concreting.
3.All reinforced concrete to be Class 30 mix and blinding concrete to be Class 15 mix.
4. Only figured dimensions to be taken from this drawing.
5. Any descripancy indimensions to be reported to the project consultants i.e architect or engineer.

6. Symbols; T-TMT Rebars to BS 4461: T - Top face
B - Bottom face
7. Cover to reinforcement; Slabs - 20mm,
Beams - 25mm,Columns - 40mm, Foundations -50mm
8. All structural steel be grade 43A.
9. All welds are 6mm thick.
10. All structural steel to be painted with anti-rust primmer paint.

Client
MINISTRY OF LANDS, PUBLIC WORKS, HOUSING AND URBAN DEVELOPMENT

STATE DEPARTMENT FOR HOUSING AND URBAN DEVELOPMENT

STRUCTURAL ENGINEER:

E.P.L

Designed by: H.I.H | *Checked by: G.N.M*

Approved by: SECRETARY, HOUSING DEPARTMENT

Date: 28TH MARCH 2026 | *Scale: As shown*


Drawing Number: 340 PAX HOSTEL/S04

Project
AFFORDABLE HOUSING G+4_340 PAX HOSTEL STRUCTURAL DRAWINGS (FRAME)

Title
TYPICAL RC SLAB DETAILS

Revisions

No.	Description	Date

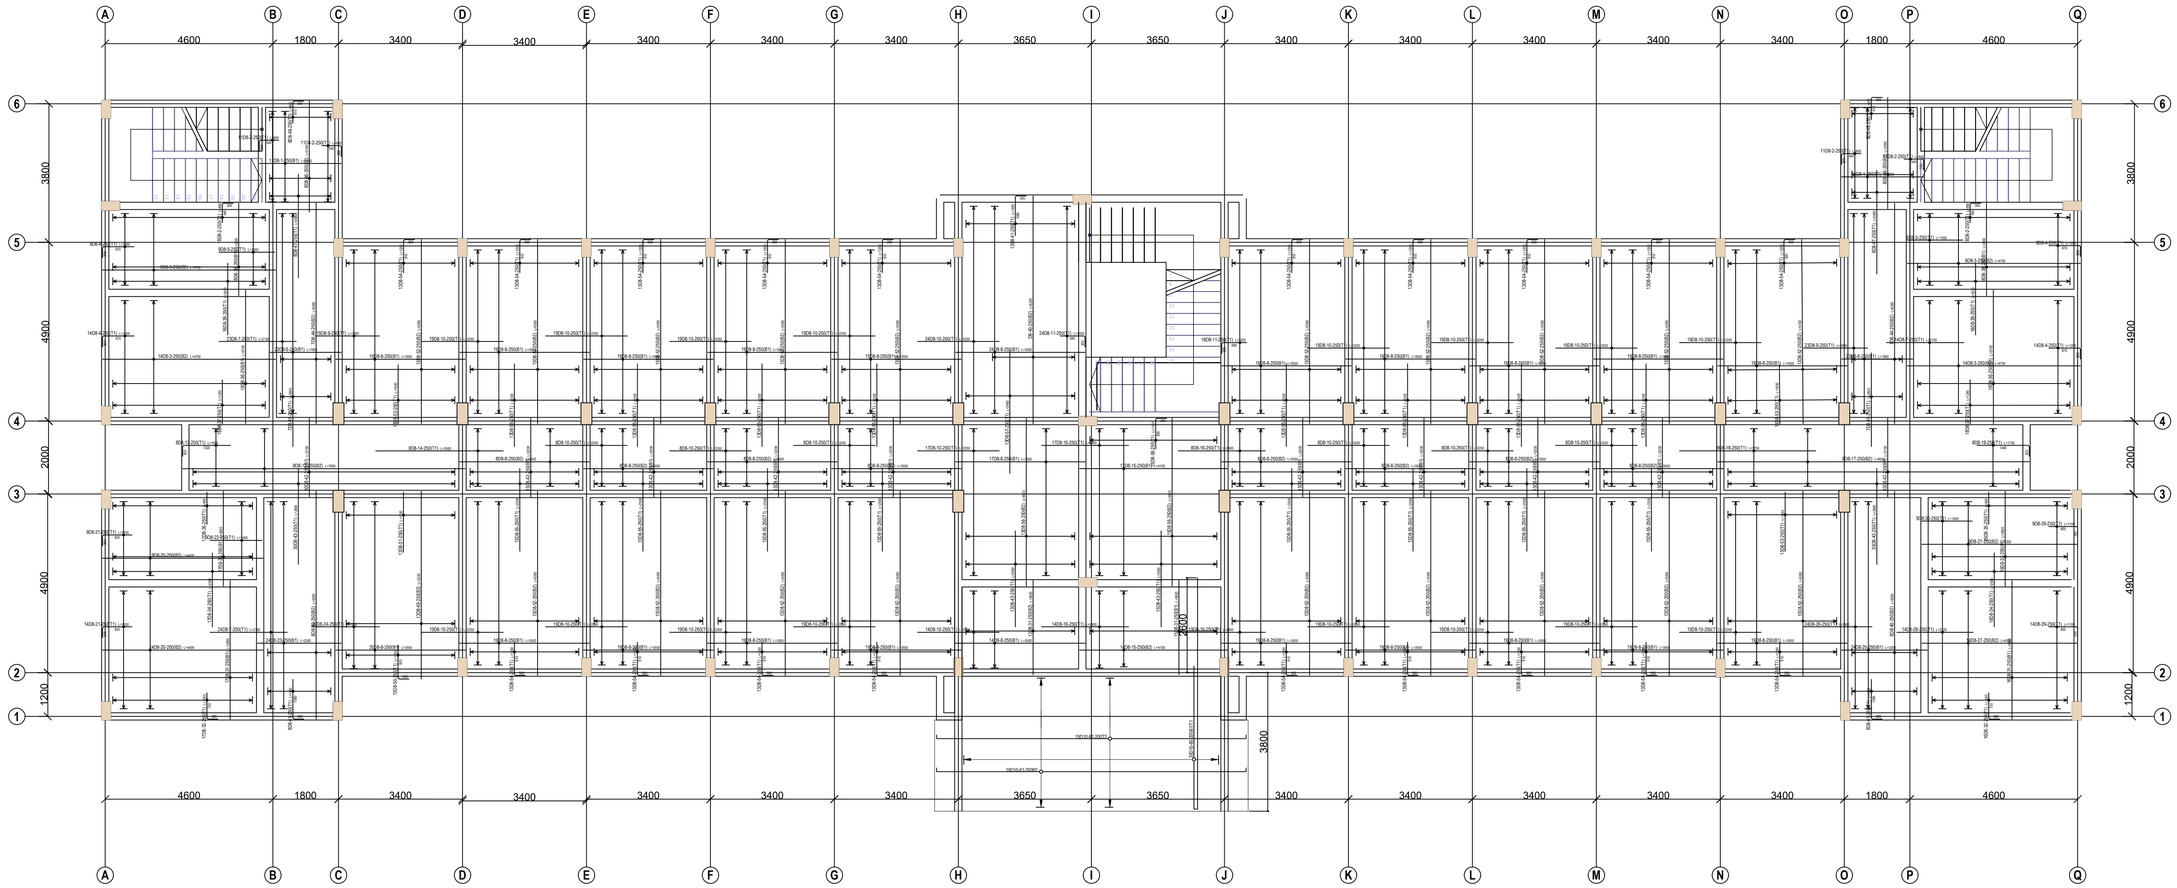

TYPICAL 1st FLOOR RC SLAB DETAILS

NOTE:

1. This design is valid for soils with low bearing capacity (75 - 125 kN/m^2).

NOTES
1. All dimensions are in millimetres unless otherwise stated.
2. All reinforcements must be checked and approved by project structural engineer prior to concreting.
3.All reinforced concrete to be Class 30 mix and blinding concrete to be Class 15 mix.
4. Only figured dimensions to be taken from this drawing.
5. Any descripancy indimensions to be reported to the project consultants i.e architect or engineer.

6. Symbols; T-TMT Rebars to BS 4461: T - Top face B - Bottom face
7. Cover to reinforcement; Slabs - 20mm, Beams - 25mm,Columns - 40mm, Foundations -50mm
8. All structural steel be grade 43A.
9. All welds are 6mm thick.
10. All structural steel to be painted with anti-rust primmer paint.

Client
MINISTRY OF LANDS, PUBLIC WORKS, HOUSING AND URBAN DEVELOPMENT
STATE DEPARTMENT FOR HOUSING AND URBAN DEVELOPMENT

STRUCTURAL ENGINEER:
E.P.L


Designed by: H.I.H | *Checked by: G.N.M*
Approved by: SECRETARY, HOUSING DEPARTMENT
Date: 28TH MARCH 2026 | *Scale: As shown*
Drawing Number: 580 PAX HOSTEL/S04


Project
AFFORDABLE HOUSING G+4_340 PAX HOSTEL STRUCTURAL DRAWINGS (FRAME)


Title
TYPICAL 1st FLOOR RC SLAB DETAILS


Revisions


No.	Description	Date

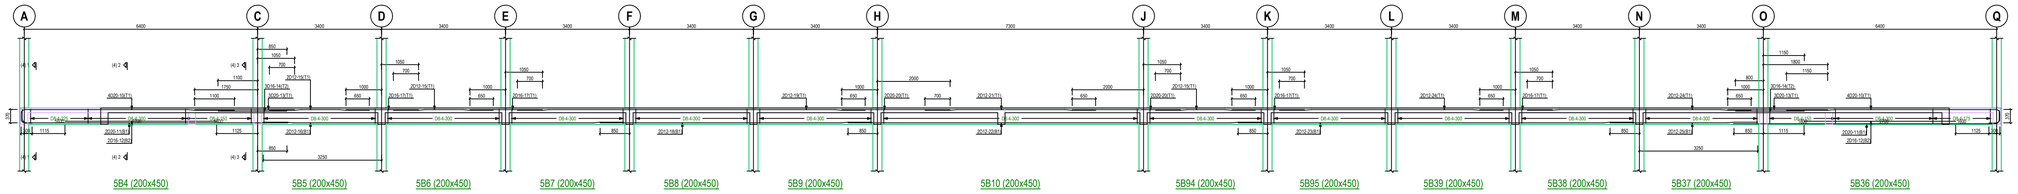


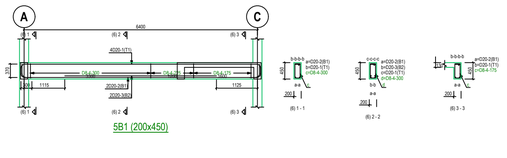


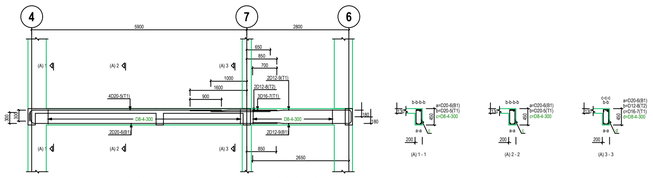


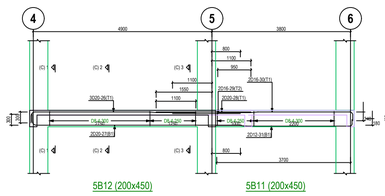


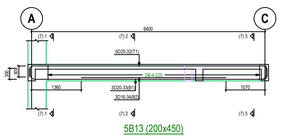


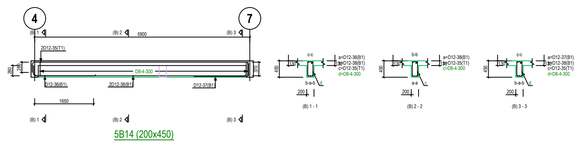


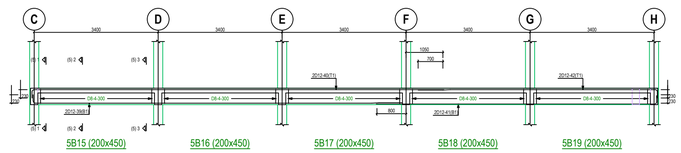


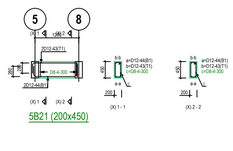


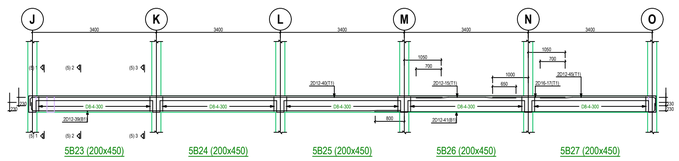


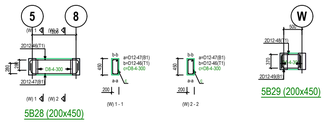


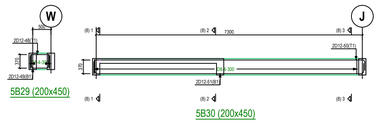


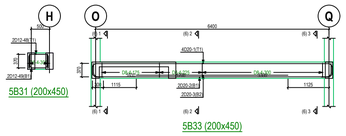


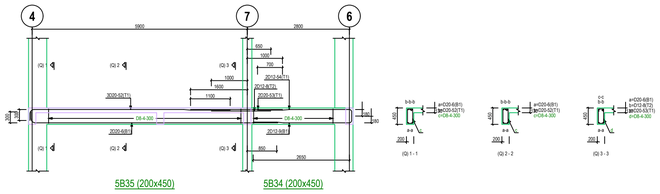

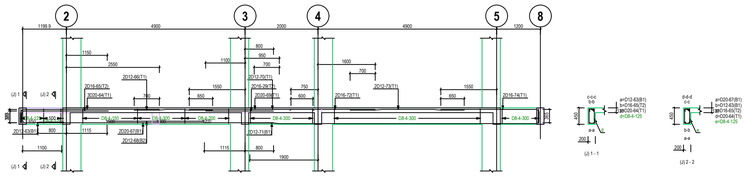

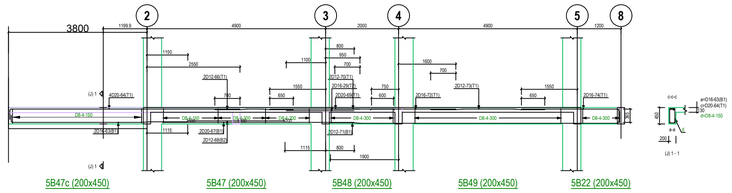

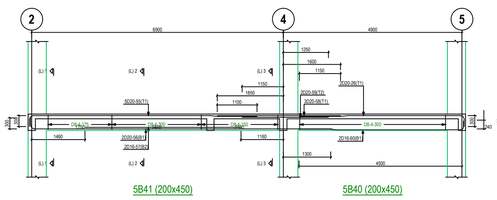

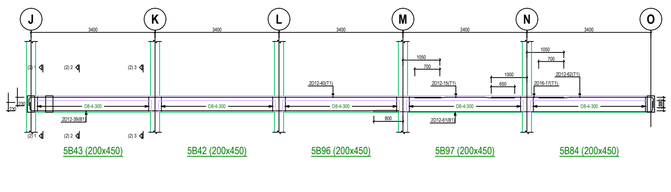

NOTE:

1. THIs design is valid for soils with low bearing capacity (75 - 125 kN/m^2).

NOTES
1. All dimensions are in millimetres unless otherwise stated.
2. All reinforcements must be checked and approved by project structural engineer prior to concreting.
3.All reinforced concrete to be Class 30 mix and blinding concrete to be Class 15 mix.
4. Only figured dimensions to be taken from this drawing.
5. Any descripancy indimensions to be reported to the project consultants i.e architect or engineer.

6. Symbols; T-TMT Rebars to BS 4461: T - Top face
B - Bottom face
7. Cover to reinforcement; Slabs - 20mm, Beams - 25mm,Columns - 40mm, Foundations -50mm
8. All structural steel be grade 43A.
9. All welds are 6mm thick.
10. All structural steel to be painted with anti-rust primmer paint.

Client
MINISTRY OF LANDS, PUBLIC WORKS, HOUSING AND URBAN DEVELOPMENT
STATE DEPARTMENT FOR HOUSING AND URBAN DEVELOPMENT

STRUCTURAL ENGINEER:
E.P.L


Designed by: H.I.H | *Checked by: G.N.M*
Approved by: SECRETARY, HOUSING DEPARTMENT
Date: 28TH MARCH 2026 | *Scale: As shown*
Drawing Number: 340 PAX HOSTEL/S05

Project
AFFORDABLE HOUSING G+4_340 PAX HOSTEL STRUCTURAL DRAWINGS (FRAME)

Title
RC BEAM DETAILS 1


Revisions

No.	Description	Date

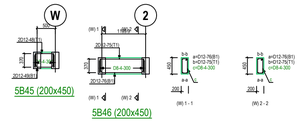


5B45 (200x450)


5B46 (200x450)

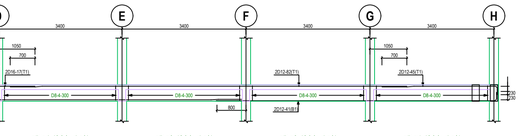

5B55 (200x450)

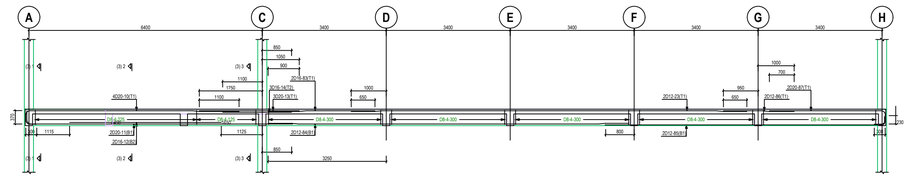


5B58 (200x450)

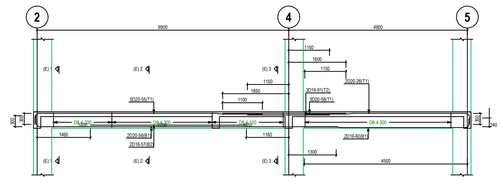

5B62 (200x450)

5B71 (200x450)

5B76 (200x450)

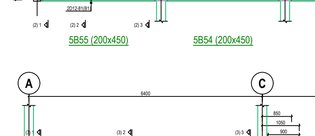


5B81 (200x450)

5B54 (200x450)


5B85 (200x450)

5B63 (200x450)

5B72 (200x450)

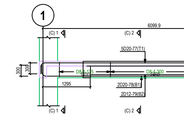

5B77 (200x450)

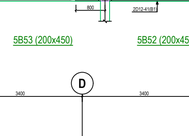

5B82 (200x450)

5B50 (200x450)

5B53 (200x450)


5B86 (200x450)

5B64 (200x450)


5B78 (200x450)

5B80 (200x450)


5B83 (200x450)

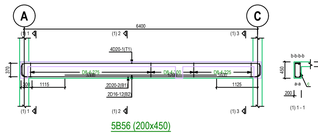

5B56 (200x450)

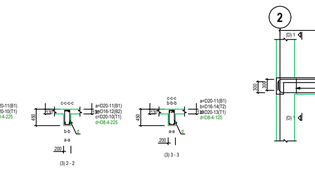

5B87 (200x450)

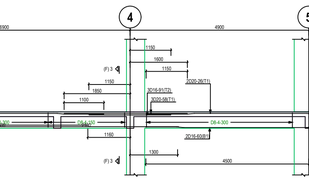


5B65 (200x450)

5B75 (200x450)


5B79 (200x450)




5B84 (200x450)

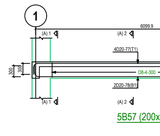

5B57 (200x450)

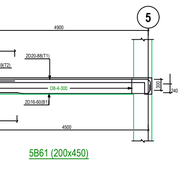


5B59 (200x450)

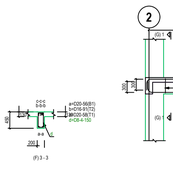


5B66 (200x450)

5B73 (200x450)


5B74 (200x450)

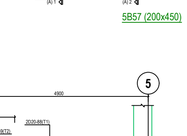


5B88 (200x450)

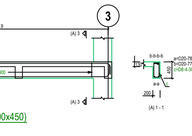

5B61 (200x450)

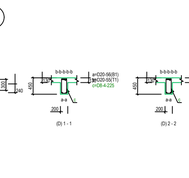

5B67 (200x450)

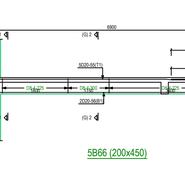

5B60 (200x450)

5B89 (200x450)

5B70 (200x450)



NOTE:

1. THIs design is valid for soils with low bearing capacity (75 - 125 kN/m^2).

NOTES
1. All dimensions are in millimetres unless otherwise stated.
2. All reinforcements must be checked and approved by project structural engineer prior to concreting.
3.All reinforced concrete to be Class 30 mix and blinding concrete to be Class 15 mix.
4. Only figured dimensions to be taken from this drawing.
5. Any descripancy indimensions to be reported to the project consultants i.e architect or engineer.

6. Symbols; T-TMT Rebars to BS 4461: T - Top face
B - Bottom face
7. Cover to reinforcement; Slabs - 20mm,
Beams - 25mm,Columns - 40mm, Foundations -50mm
8. All structural steel be grade 43A.
9. All welds are 6mm thick.
10. All structural steel to be painted with anti-rust primmer paint.

Client
MINISTRY OF LANDS, PUBLIC WORKS, HOUSING AND URBAN DEVELOPMENT

STATE DEPARTMENT FOR HOUSING AND URBAN DEVELOPMENT

STRUCTURAL ENGINEER:

E.P.L

Designed by: H.I.H | *Checked by: G.N.M*

Approved by: SECRETARY, HOUSING DEPARTMENT

Date: 28TH MARCH 2026 | *Scale: As shown*


Drawing Number: 340 PAX HOSTEL/S06

Project
AFFORDABLE HOUSING G+4_340 PAX
HOSTEL STRUCTURAL DRAWINGS (FRAME)


Title
RC BEAM DETAILS 2

Revisions


No.	Description	Date

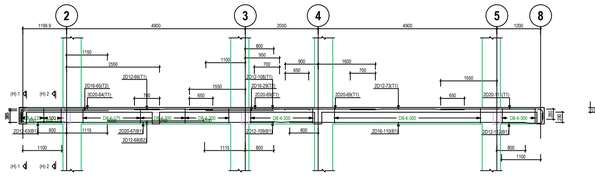


5B90 (200x450) 5B68 (200x450) 5B69 (200x450) 5B70 (200x450) 5B20 (200x450)

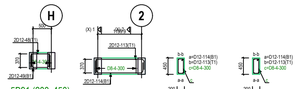


5B91 (200x450) 5B92 (200x450)

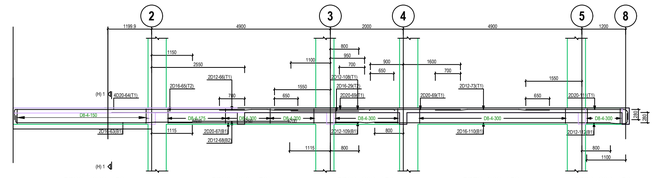


5B68c (200x450) 5B68 (200x450) 5B69 (200x450) 5B70 (200x450) 5B20 (200x450)

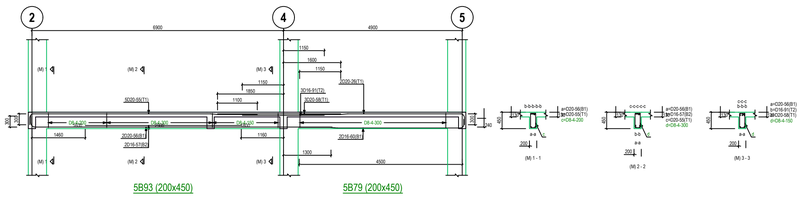


5B93 (200x450) 5B79 (200x450)

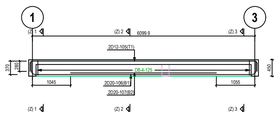


5B98 (200x450)

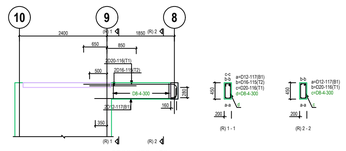


5B99 (200x450)

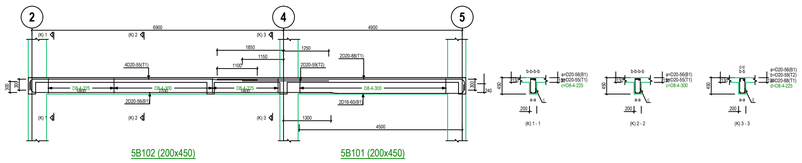


5B102 (200x450) 5B101 (200x450)

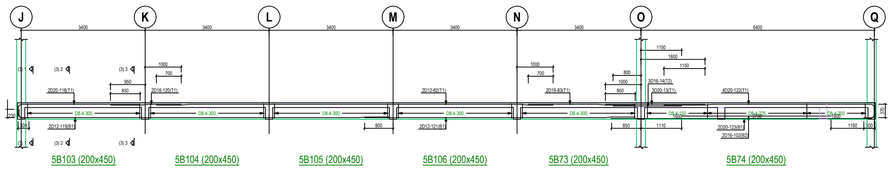


5B103 (200x450) 5B104 (200x450) 5B105 (200x450) 5B106 (200x450) 5B73 (200x450) 5B74 (200x450)

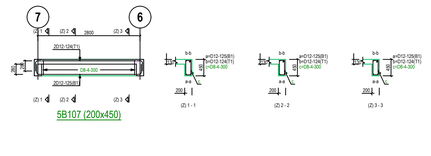


5B107 (200x450)

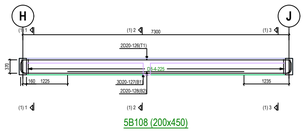


5B108 (200x450)

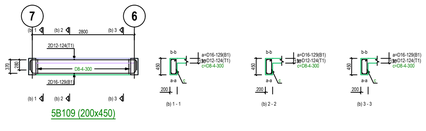


5B109 (200x450)

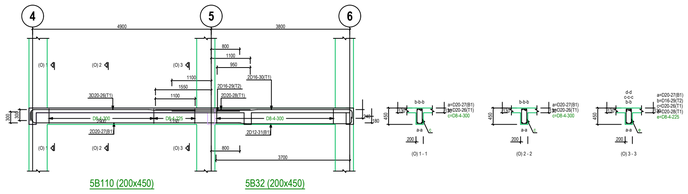


5B110 (200x450) 5B32 (200x450)

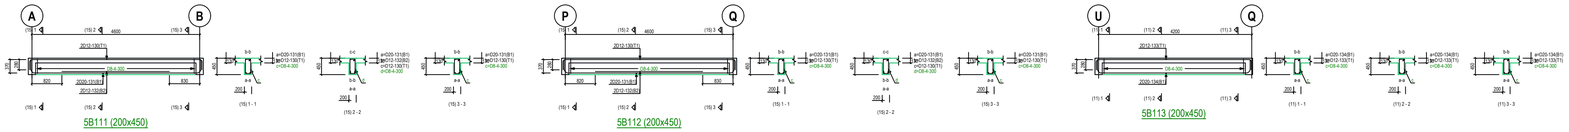

5B111 (200x450) 5B112 (200x450) 5B113 (200x450)

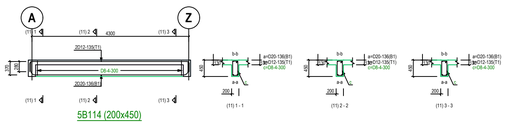

5B114 (200x450)

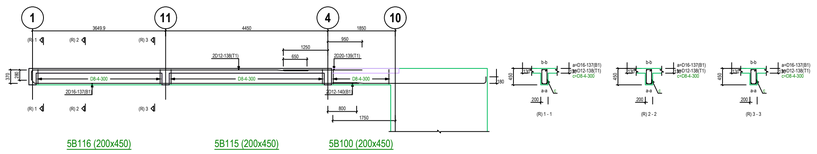

5B116 (200x450) 5B115 (200x450) 5B100 (200x450)

NOTES

1. All dimensions are in millimetres unless otherwise stated.
2. All reinforcements must be checked and approved by project structural engineer prior to concreting.
3. All reinforced concrete to be Class 30 mix and blinding concrete to be Class 15 mix.
4. Only figured dimensions to be taken from this drawing.
5. Any descripancy indimensions to be reported to the project consultants i.e architect or engineer.

6. Symbols; T-TMT Rebars to BS 4461: T - Top face
   B - Bottom face
7. Cover to reinforcement; Slabs - 20mm,
Beams - 25mm,Columns - 40mm, Foundations -50mm
8. All structural steel be grade 43A.
9. All welds are 6mm thick.
10. All structural steel to be painted with anti-rust primmer paint.

Client
MINISTRY OF LANDS, PUBLIC WORKS, HOUSING AND URBAN DEVELOPMENT

STATE DEPARTMENT FOR HOUSING AND URBAN DEVELOPMENT

STRUCTURAL ENGINEER:

E.P.L

Designed by: H.I.H | *Checked by: G.N.M*

Approved by: SECRETARY, HOUSING DEPARTMENT

Date: 28TH MARCH 2026 | *Scale: As shown*

Drawing Number: 340 PAX HOSTEL/S07

Project
AFFORDABLE HOUSING G+4_340 PAX HOSTEL STRUCTURAL DRAWINGS (FRAME)


Title
RC BEAM DETAILS 3

Revisions

No.	Description	Date

NOTE:


1. THIs design is valid for soils with low bearing capacity (75 - 125 kN/m^2).

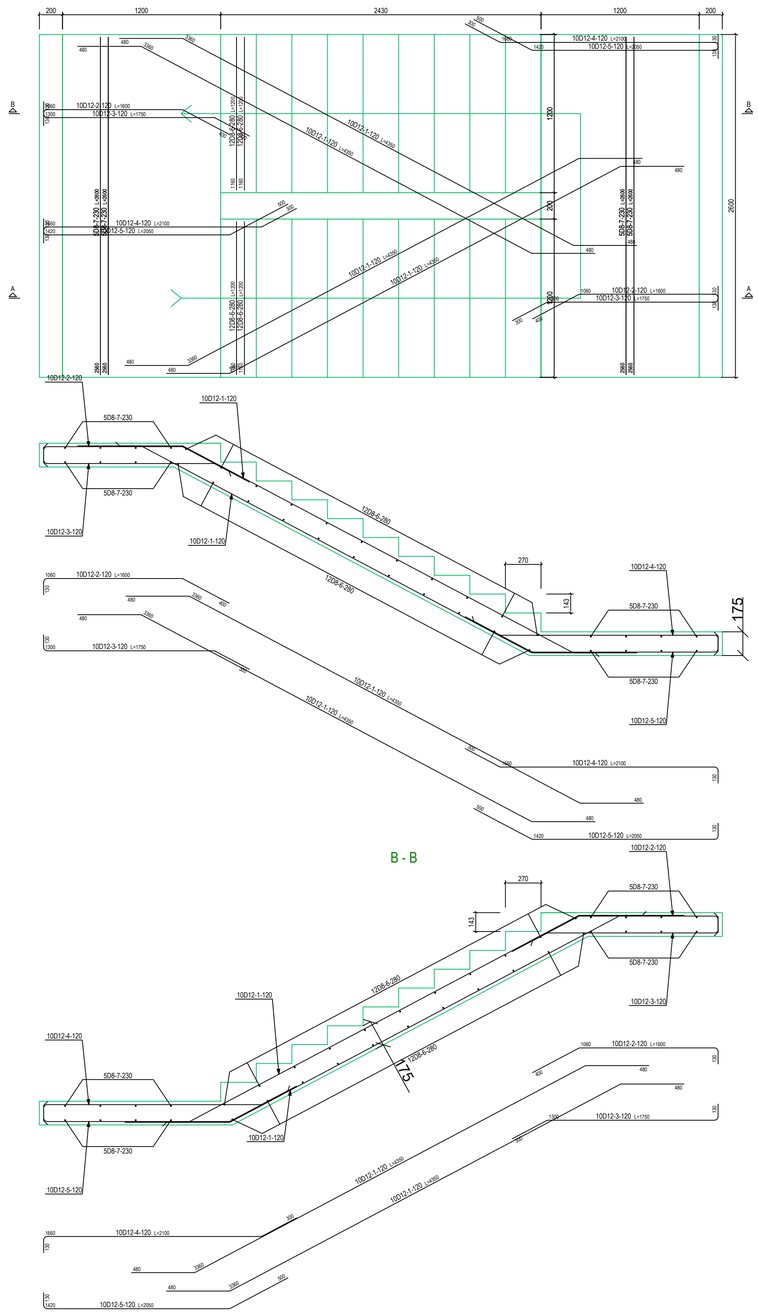


B - B

A - A

M1 Stairs Detail (Scale: 1/20)

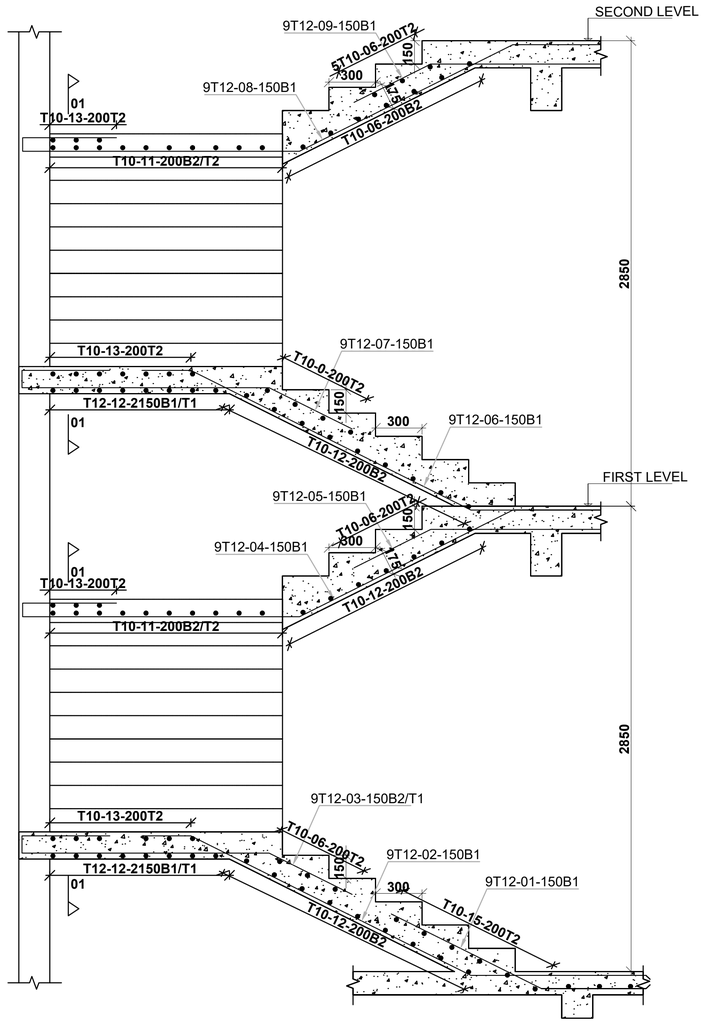

STAIRCASE 1-SECTION
175mm Thick Solid Waist
Scale 1:25

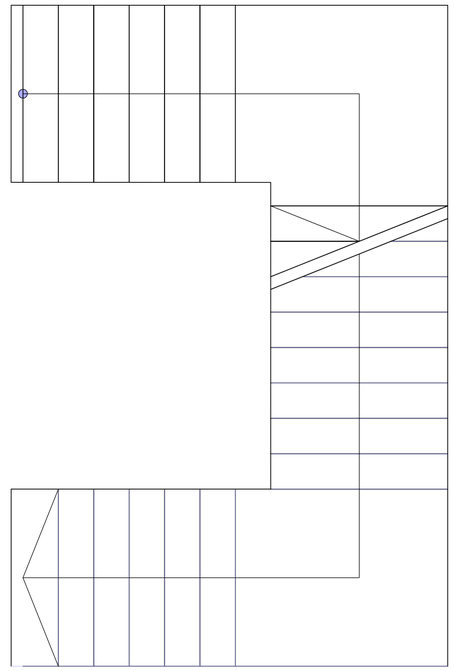

OVERALL STAIRCASE SECTION

NOTE:

1. Thls design is valid for soils with low bearing capacity (75 - 125 kN/m^2).

NOTES
1. All dimensions are in millimetres unless otherwise stated.
2. All reinforcements must be checked and approved by project structural engineer prior to concreting.
3.All reinforced concrete to be Class 30 mix and blinding concrete to be Class 15 mix.
4. Only figured dimensions to be taken from this drawing.
5. Any descripancy indimensions to be reported to the project consultants i.e architect or engineer.

6. Symbols; T-TMT Rebars to BS 4461: T - Top face, B - Bottom face
7. Cover to reinforcement; Slabs - 20mm, Beams - 25mm,Columns - 40mm, Foundations -50mm
8. All structural steel be grade 43A.
9. All welds are 6mm thick.
10. All structural steel to be painted with anti-rust primmer paint.

Client
MINISTRY OF LANDS, PUBLIC WORKS, HOUSING AND URBAN DEVELOPMENT
STATE DEPARTMENT FOR HOUSING AND URBAN DEVELOPMENT


STRUCTURAL ENGINEER:
E.P.L

Designed by: H.I.H | *Checked by: G.N.M*
Approved by: SECRETARY, HOUSING DEPARTMENT
Date: 28TH MARCH 2026 | *Scale: As shown*
Drawing Number: 340 PAX HOSTEL/S09


Project
AFFORDABLE HOUSING G+4_340 PAX HOSTEL STRUCTURAL DRAWINGS (FRAME)

Title
STAIRCASE DETAILS


Revisions		
No.	Description	Date

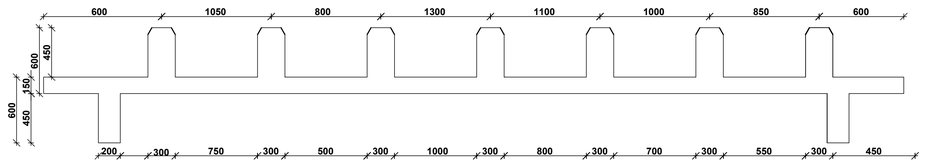


WATER TANK BEARER BEAMS
SECTION 150mm SOLID SLAB
SCALE 1:25

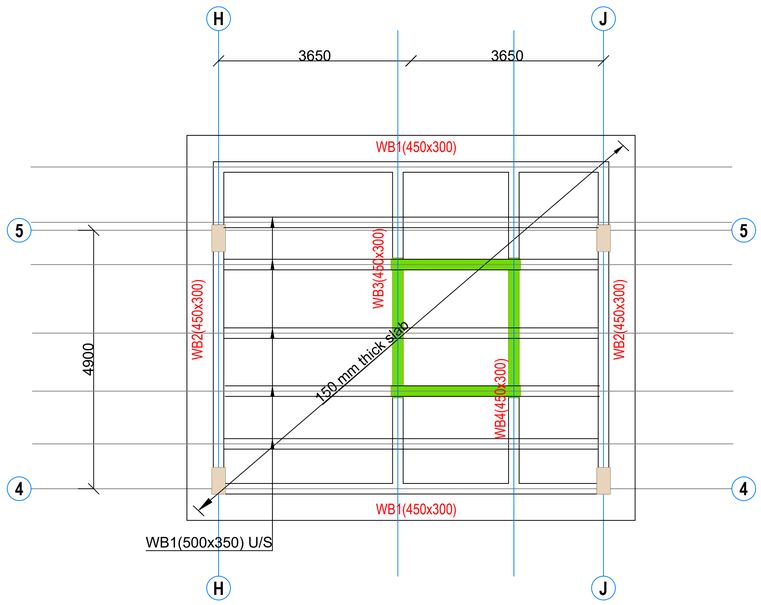


WATER TANK BEAM AND SLAB LAYOUT

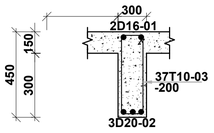


WB1-450x300
2NO.
SCALE 1:25

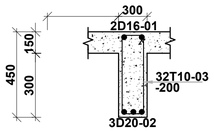


WB2-450x300
2NO.
SCALE 1:25

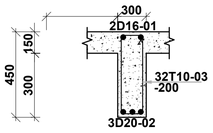


WB3-450x300
1NO.
SCALE 1:25

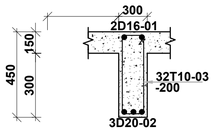


WB4-450x300
2NO.
SCALE 1:25

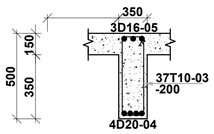

WB1-500x350 U/S
5NO.
SCALE 1:25

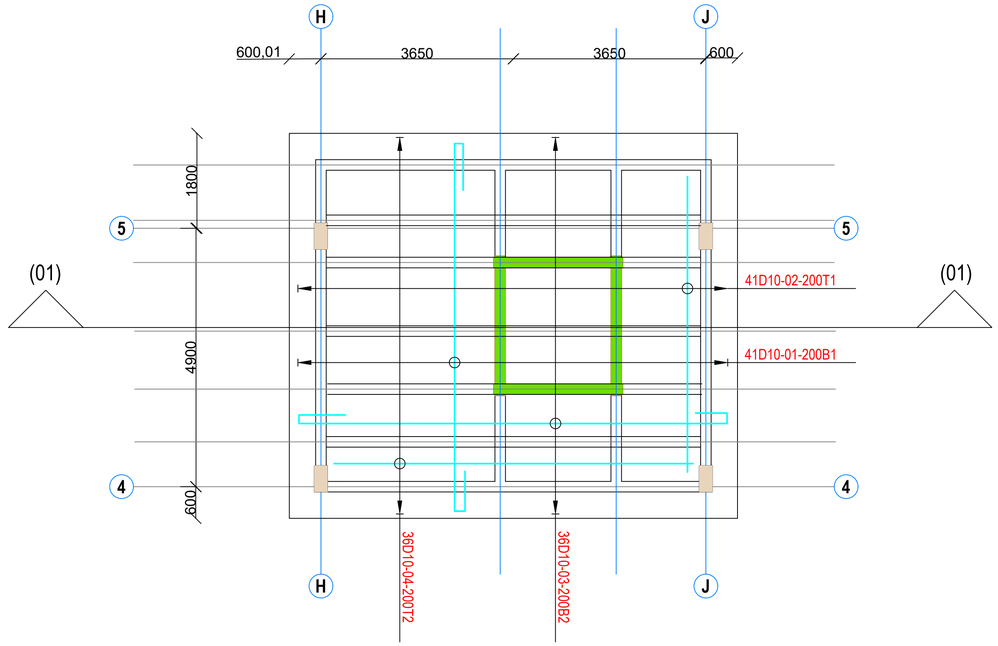

WATER TANK RC SLAB DETAILS

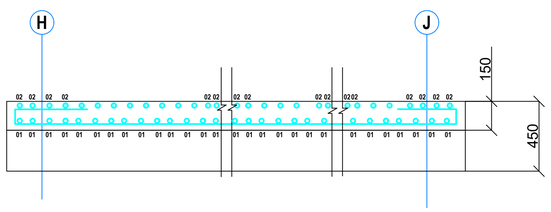

SECTION (01)-(01)

NOTES
1. All dimensions are in millimetres unless otherwise stated.
2. All reinforcements must be checked and approved by project structural engineer prior to concreting.
3.All reinforced concrete to be Class 30 mix and blinding concrete to be Class 15 mix.
4. Only figured dimensions to be taken from this drawing.
5. Any descripancy indimensions to be reported to the project consultants i.e architect or engineer.

6. Symbols; T-TMT Rebars to BS 4461: T - Top face
B - Bottom face
7. Cover to reinforcement; Slabs - 20mm,
Beams - 25mm,Columns - 40mm, Foundations -50mm
8. All structural steel be grade 43A.
9. All welds are 6mm thick.
10. All structural steel to be painted with anti-rust primmer paint.

Client
MINISTRY OF LANDS, PUBLIC WORKS, HOUSING AND URBAN DEVELOPMENT

STATE DEPARTMENT FOR HOUSING AND URBAN DEVELOPMENT

STRUCTURAL ENGINEER:
E.P.L

Designed by: H.I.H | *Checked by: G.N.M*
Approved by: SECRETARY, HOUSING DEPARTMENT
Date: 28TH MARCH 2026 | *Scale: As shown*
Drawing Number: 340 PAX HOSTEL/S10

Project
AFFORDABLE HOUSING G+4_340 PAX HOSTEL STRUCTURAL DRAWINGS (FRAME)

Title
WATER TANK DETAILS

Revisions		
No.	Description	Date